


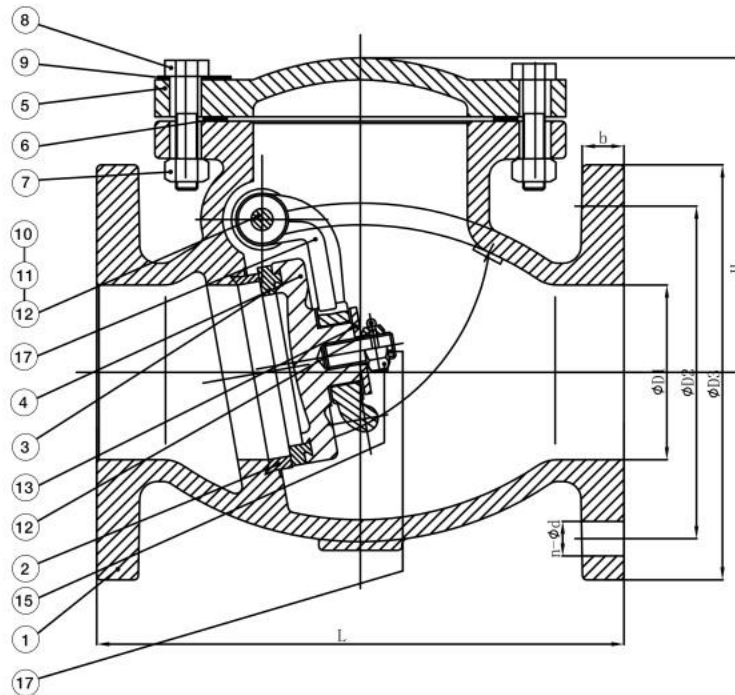

NO.	PART NAME	MATERIAL	STANDARD	NO.	PART NAME	MATERIAL	STANDARD
1	BODY	CAST IRON	ASTM A126B	10	HINGE PIN	BRASS	ASTM B16 C36000
2	SEAT RING	CAST BRONZE	ASTM B62	11	GASKET	PTFE	NON ASBESTOS
3	DISC RING	CAST BONZE	ASTM B62	12	SIDE PLUG	BRASS	ASTM B16 C36000
4	DISC	CAST IRON	ASTM B126B	13	WASHER	STEEL	ASTM A307 B
5	BONNET	CAST IRON	ASTM A126B	14	SPLIT PIN	STAINLESS STEEL	ASTM 420 S42000
6	BODY GASKET	GRAPHITE	NON ASBESTOS	15	NUT	STEEL	ASTM A307 B
7	NUTS	STEEL	ASTM A307B	16	BOLT	STEEL	ASTM A307 B
8	BOLTS	STEEL	ASTM A307B	17	HINGE	DUCTILE IRON	ASTM A536
9	NAME PLATE	ALUMINUM	COMMERCIAL				

JOINT VALVE ROUTINE & SHUTDOWN MAINTENANCE FRAGNET

OPENING	REFURBISHMENT	REFIXING
Preparation	Shop Activities	Valve return & refix
LOTO	Dismantle Valve	Rig Back
Depressurize	Clean	Fix in location
Isolate	Remove Dirt	Check direction and angle
Inspect as found	Remove Scale	Bolting
TAG	Remove product	Clean mating flange surfaces
Inspect Body	Lubricate as recommended	Replace gaskets
Inspect Bonnet	Lubricate stem	Boxup in location
Functional Check	Lubricate gearboxes	Torque to appropriate value
Manual Operation	Lubricator actuator links	Reinsulate for HOT & Cold Services
Check for Open/Close	Seal & packing	Deblind
Removal & Disassemble	Replace valve gaskets	Descaffold
Drop the Valve	Replace valve packing	
Scaffold	Replace O-rings	
Drop	Replace seals	
Move to shop	Machining if needed	
	Machine worn out parts	
	Machine gasket seats	
	Machine stem to free	
	Reassemble	
	Boxup Valve	
	Connect Body to Bonnet	
	Boltup end connections	
	Valve testing	
	Leak Test	
	Pressure test in shop	
	Painting	
	Final Visual Inspection	

rPlan AT 39, MERMAID 1 CHS LTD., SEC-11, CBD-BELAPUR, NAVI MUMBAI - 400611		Draw Purpose Code :- Status of Approval :- Dimensions as Mentioned Engg Code :- Backup Info Code :- Angle of Projection :-		Statutory Note: This document is prepared by rPlan and is the sole proprietary of the company. Its purpose is educational and no references within this document are for Engineering or Design correlation with the applicable codes. For any clarifications beyond the intended purpose viewers can always correspond to rPlan via its company website. This drw is not for duplication without company permission!	
Legal Owner 	QR Code	Draw electronic code Drawn By:		Checked Approved by Rev XX	Checked Approved Date DWG No.
Drawn Date		Description: Typ CHECK VALVE FRAGNET Preliminary Doc under prep		SCALE:- SHEET	